20'-0"

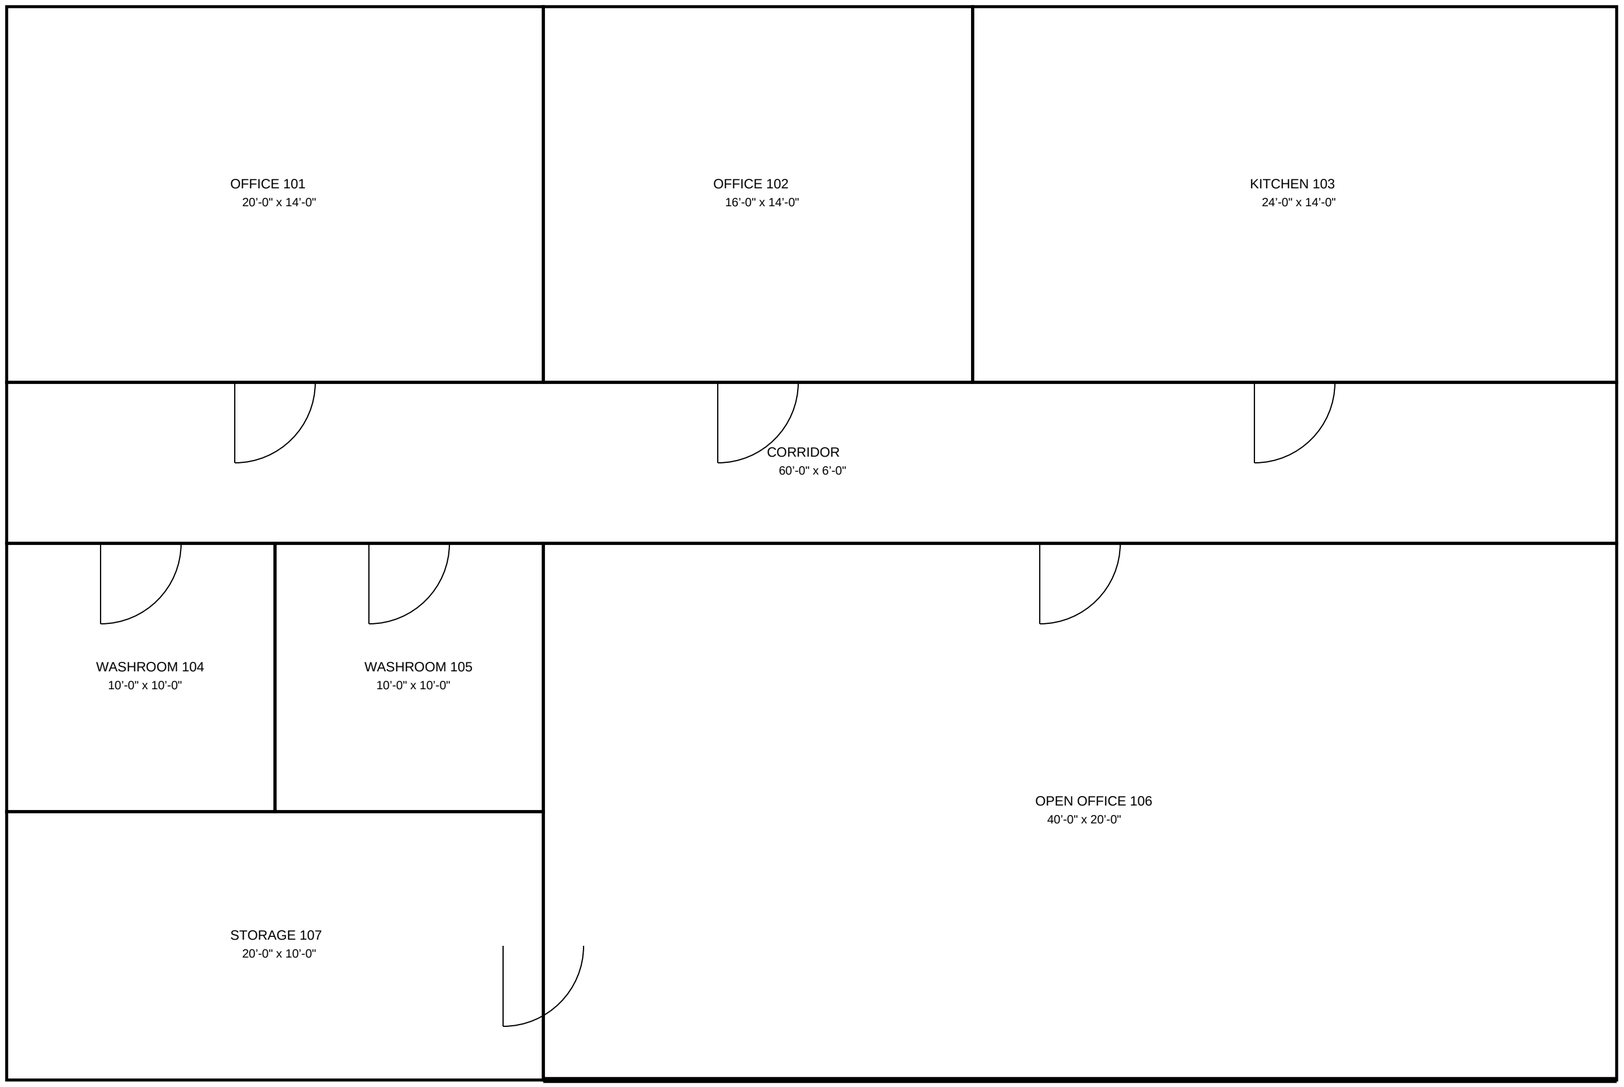

STEADFAST CONSTRUCTIONS LTD

TEST PLAN FOR THE TAKEOFF APP

FLOOR PLAN

SCALE: 1/4" = 1'-0"

NOT FOR CONSTRUCTION

SHEET

A-101

20'-0"

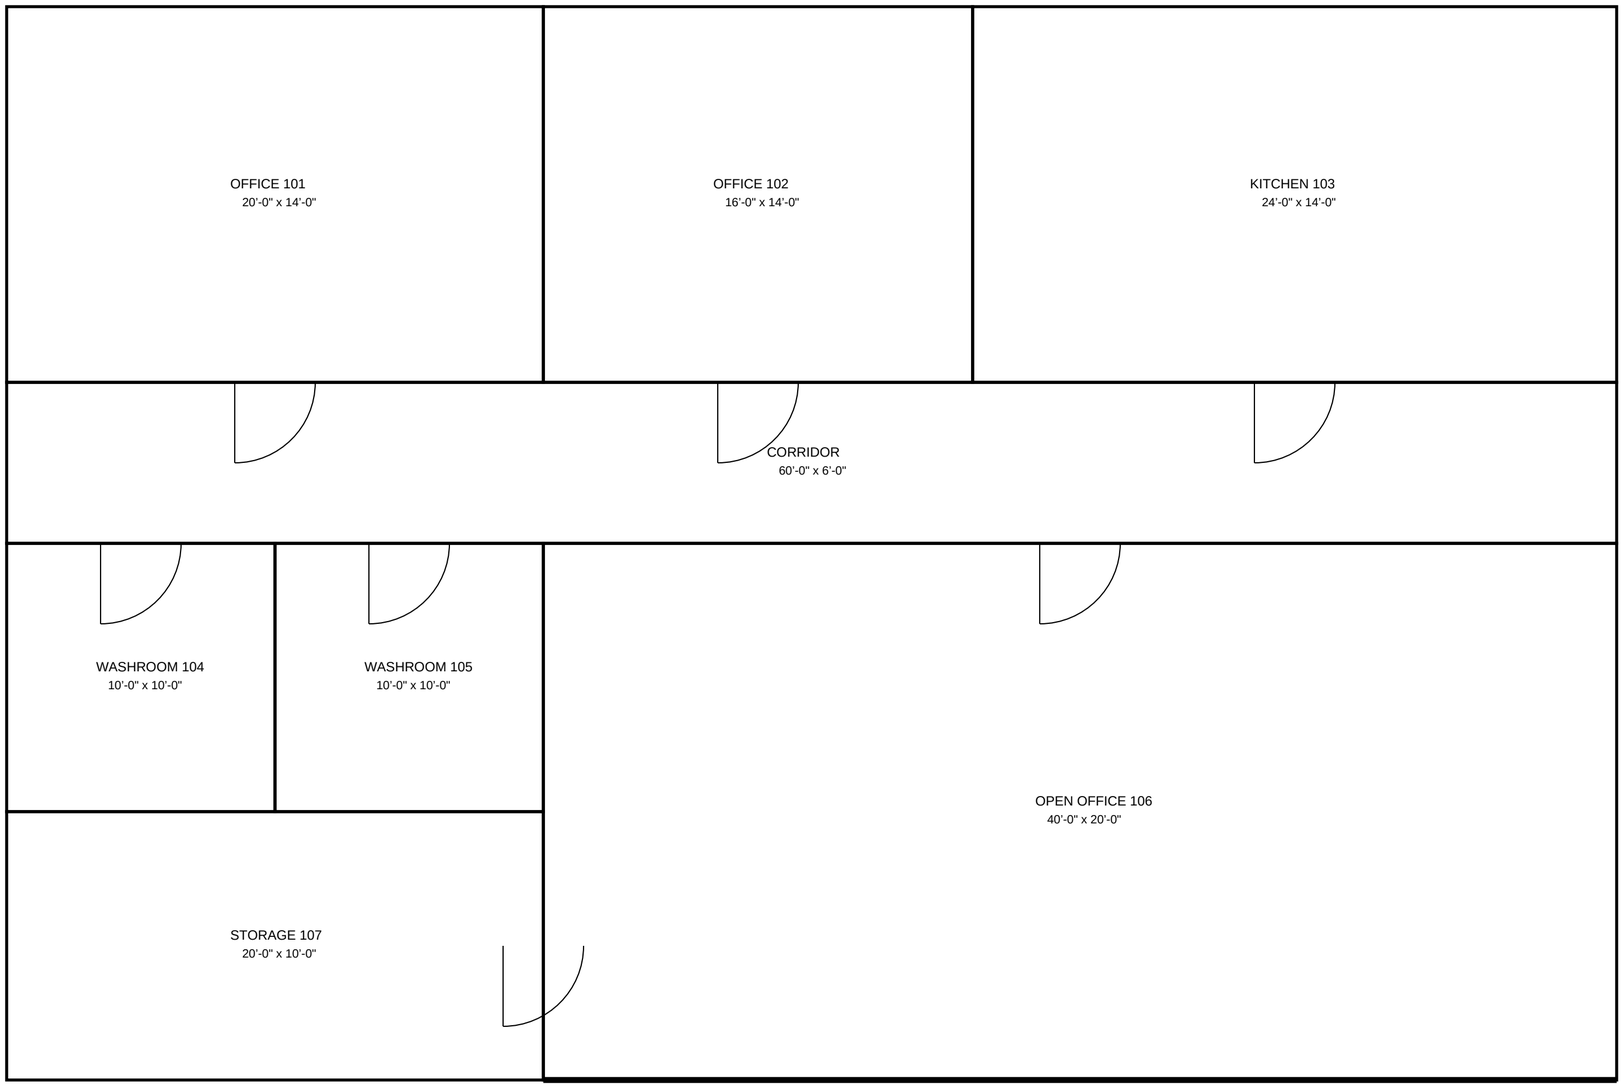

STEADFAST CONSTRUCTIONS LTD

TEST PLAN FOR THE TAKEOFF APP

FINISH PLAN

SCALE: 1/4" = 1'-0"

NOT FOR CONSTRUCTION

SHEET

A-102